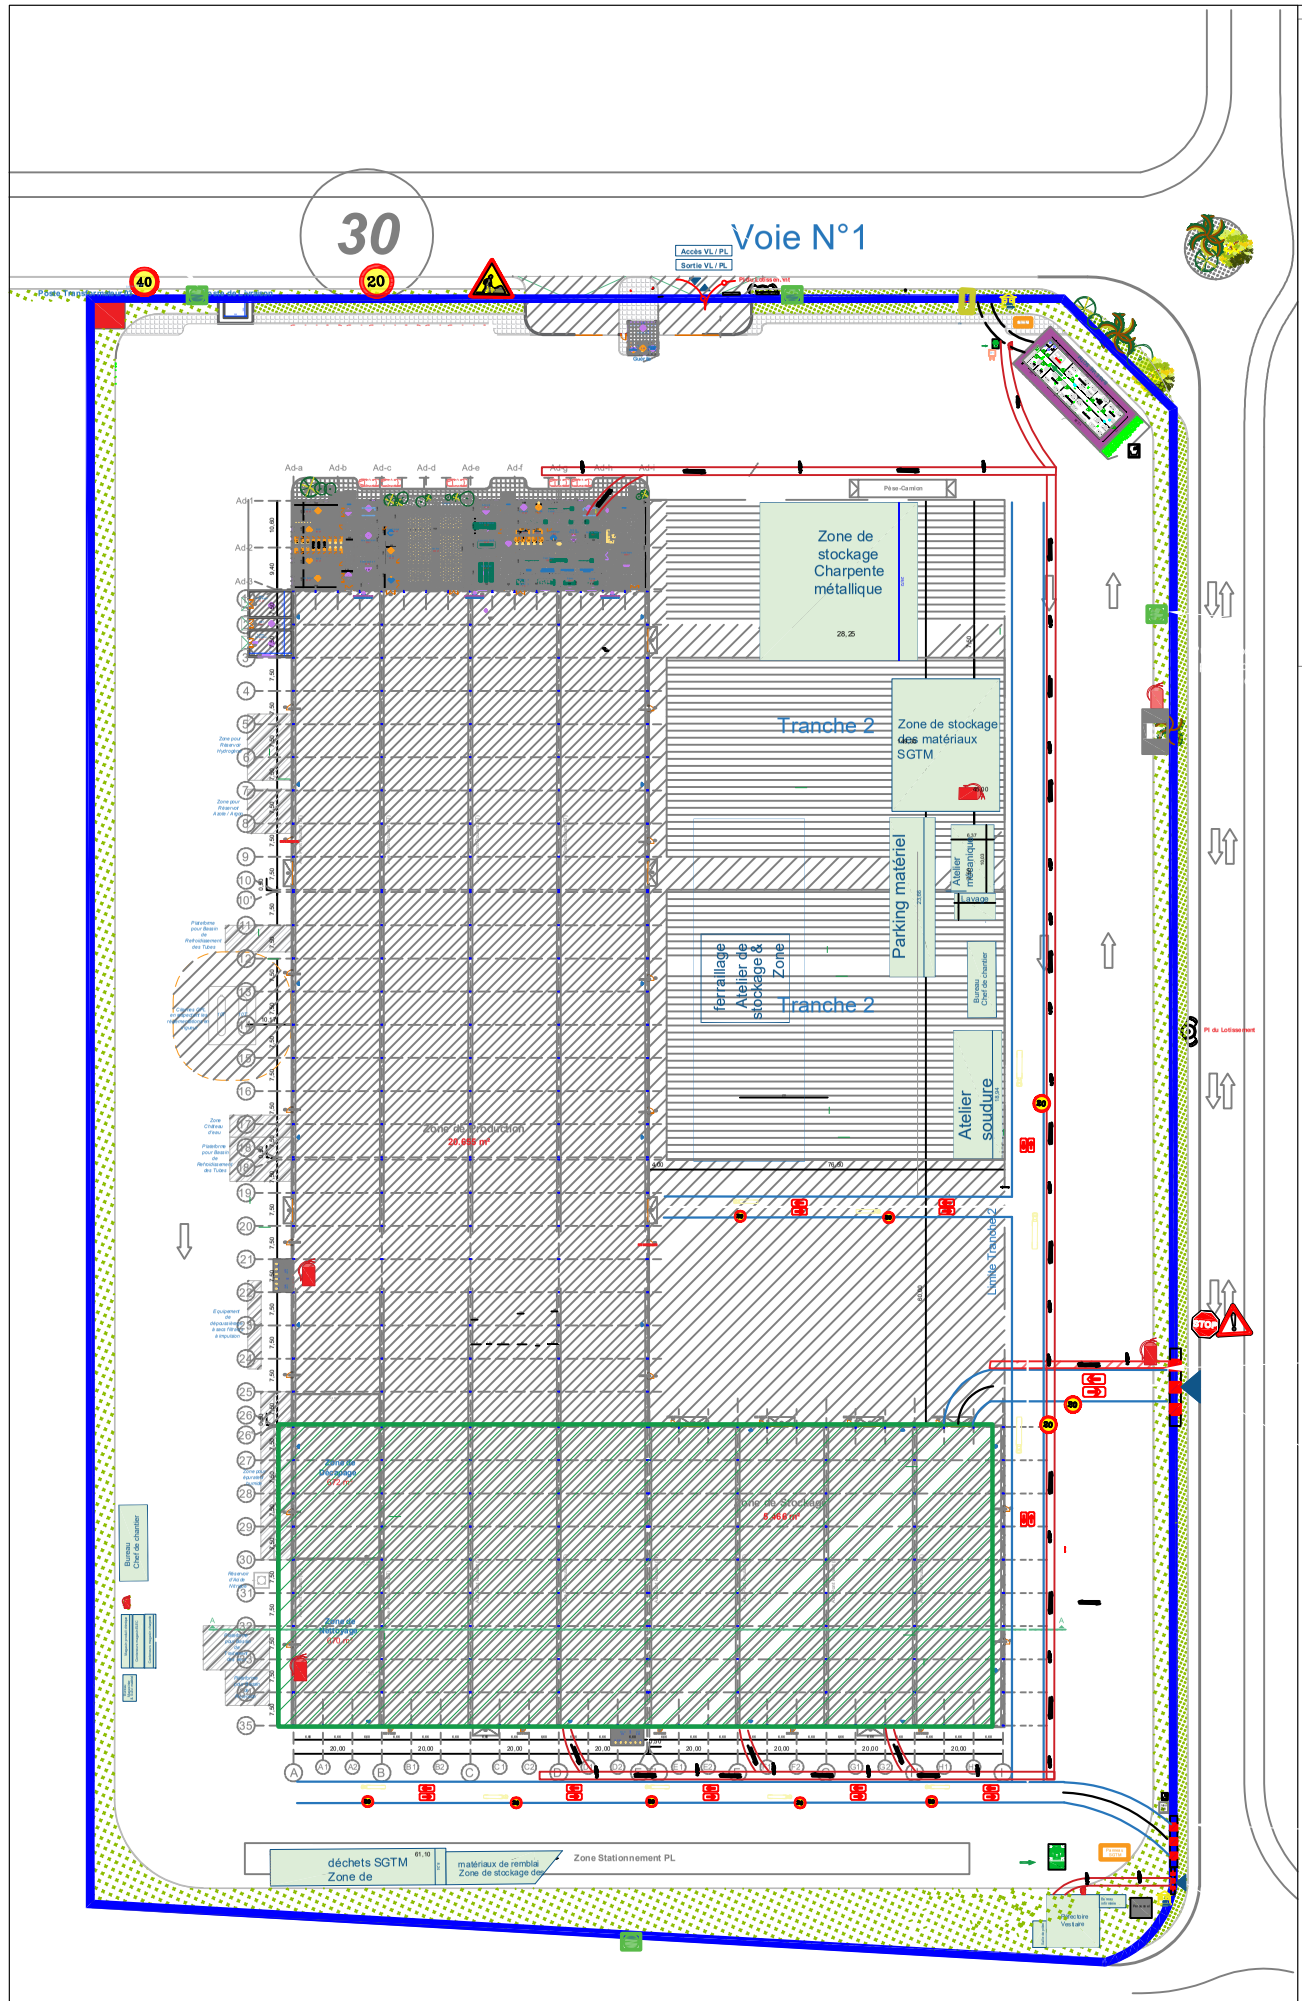

Plan RDC

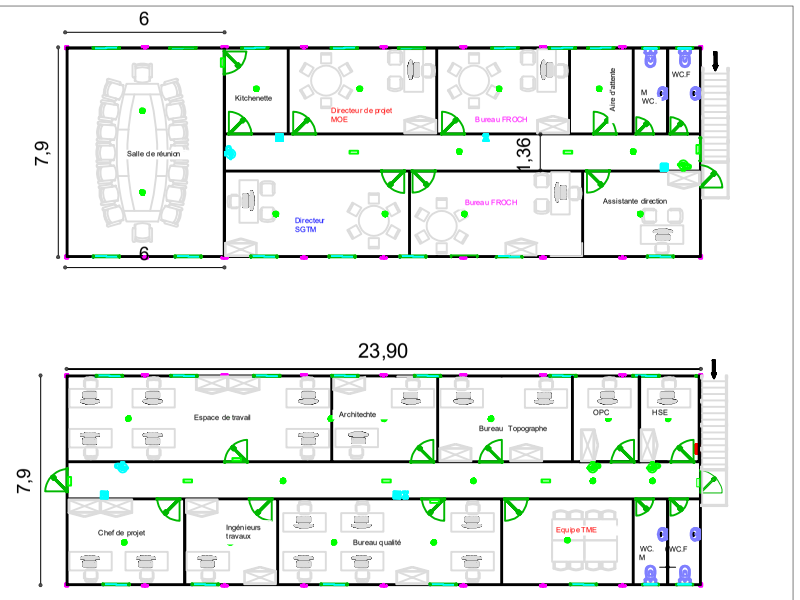

BASE VIE SGTM

LEGENDE

- Panneau SGTM
- Extincteur
- Point de rassemblement
- Guérite de gardiennage
- Sortie d'engins
- Panneau port des EPI
- Point d'eau
- Limitation de vitesse 20km/h
- STOP
- Barrière
- Limitation de vitesse 40km/h
- Sens d'évacuation
- Guérite de gardiennage
- Clôture de chantier

ROYAUME DU MAROC
Wilaya de la Région Tanger - Tétouan - Alhoceima
Préfecture/Province: Tanger - Assilah
Arouma

PROJET : CONSTRUCTION D'UNE UNITE INDUSTRIELLE
DE FABRICATION DE TUBES, TUYAUX, FEUILLES ET BOBINES EN ACIER INOXYDABLE
Tanger Tech, lots 36 et 37

Réf foncière N°	T. 76106/61 , T. 76107/61	Zonage PA	TANGER TECH

Maître d'ouvrage	Froch Stainless Morocco
ARCHITECTE AUTEUR DE L'ŒUVRE:	ARCHITECTURE PROJET Sarl Hamza NECHAR et Hamza EL BOUAMI N°Autorisation 3597 du 17/12/2012 et 3982 du 24/08/2015 Rue Al Yamane, Résidence les 47 temps. Bloc C, Bureau 32. Tanger E-mail: info@approjet.net Tél: 05 39 32 14 48 Cachet et signature

Planche N°	1	2	Plan d'instalation de chantier
Version N°	1		

Index des Planches

N°	Descriptions	ECHELLE	N°	Descriptions	ECHELLE
1/2	Repérage Faux Plafond	1/50			
2/2	Repérage Faux Plafond	1/200			

Cadre réservé à l'administration Reçu le ...../...../2024 Sous le N° .....